

Welcome - this is a real drawing.

Mark it up. Measure it. Nothing here is a mock-up, and nothing you do to it can hurt anything.

1 Draw a revision cloud

Pick the cloud tool and drag a box around something. Give it a subject and a discipline in the panel on the right.

2 Calibrate the scale

Turn to page 2 and calibrate against the dimension printed there - it reads 144'-0". Then measure the building width.

3 Check the answer

The width is printed on the sheet. If your measurement agrees, the scale is right. That is the habit worth forming.

4 Filter the markup list

Add a few markups with different disciplines, then filter. The drawing dims everything you filtered out.

5 Export the summary

Export, then Summary (XLSX). Three sheets: the register, the takeoff with its provenance, and a roll-up by cost code.

Your markups are saved as you draw. There is no Save button; the status bar tells you the state.

This sheet lives in Documents/SheetForge. Delete that folder and it is gone - nothing is kept anywhere else.

No account, no cloud, no telemetry. The application makes no network request unless you ask it to check for an update.

MARKUP LEGEND



Revision cloud

An RFI, a clash, anything that needs an answer from somebody else.



Measurement

Carries its scale, its calibration and the raw page length with it, so it can be checked later.



Text and callouts

Notes that belong to the review rather than to the drawing.

Every markup is a record with an author, a timestamp and a status - never ink burnt into the PDF.

What you are looking at

The keyed notes on the left refer to these parts of the workspace.

SheetForge

Open PDF

Export

DRAWINGS

A-201

A-202

M-401

S-101

RFI 014 - clash

148'-6"

MARKUP


Subject

Discipline

Cost code

Status

Quantity

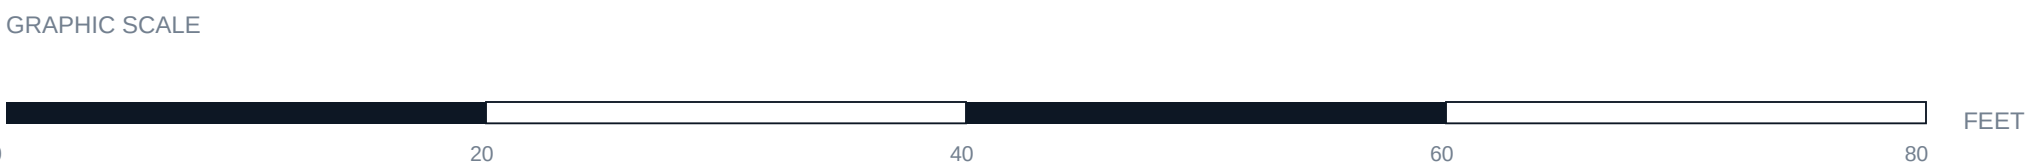

SheetForge

Construction drawing review

PROJECT

Tutorial - Riverside Tower

DRAWN BY

SheetForge

SCALE

1/8" = 1'-0"

DATE

Issued with this build

STATUS

Not for construction



REVISIONS		
REV	DATE	DESCRIPTION
A	-	Issued with the application

T-101

GETTING STARTED

Practice sheet

Calibrate against the 144'-0" dimension below the plan, then measure the far side. It should read 96'-0".
Measure the OPEN OFFICE as an area and you should get 2,304 SF - the number printed inside it.
If either answer disagrees, the calibration is wrong rather than the sheet. Set it again and check.

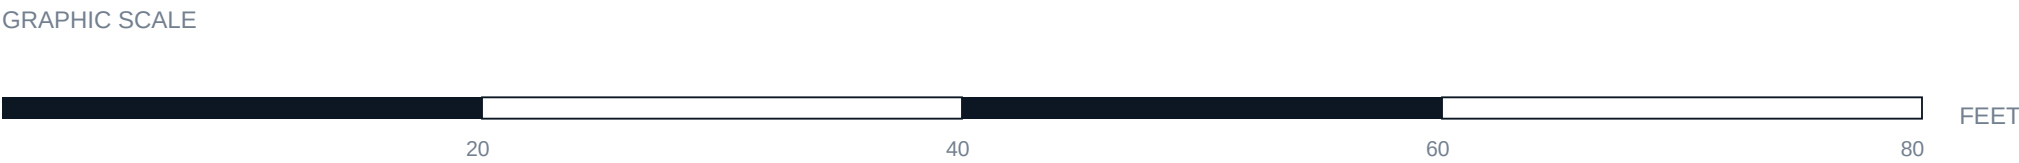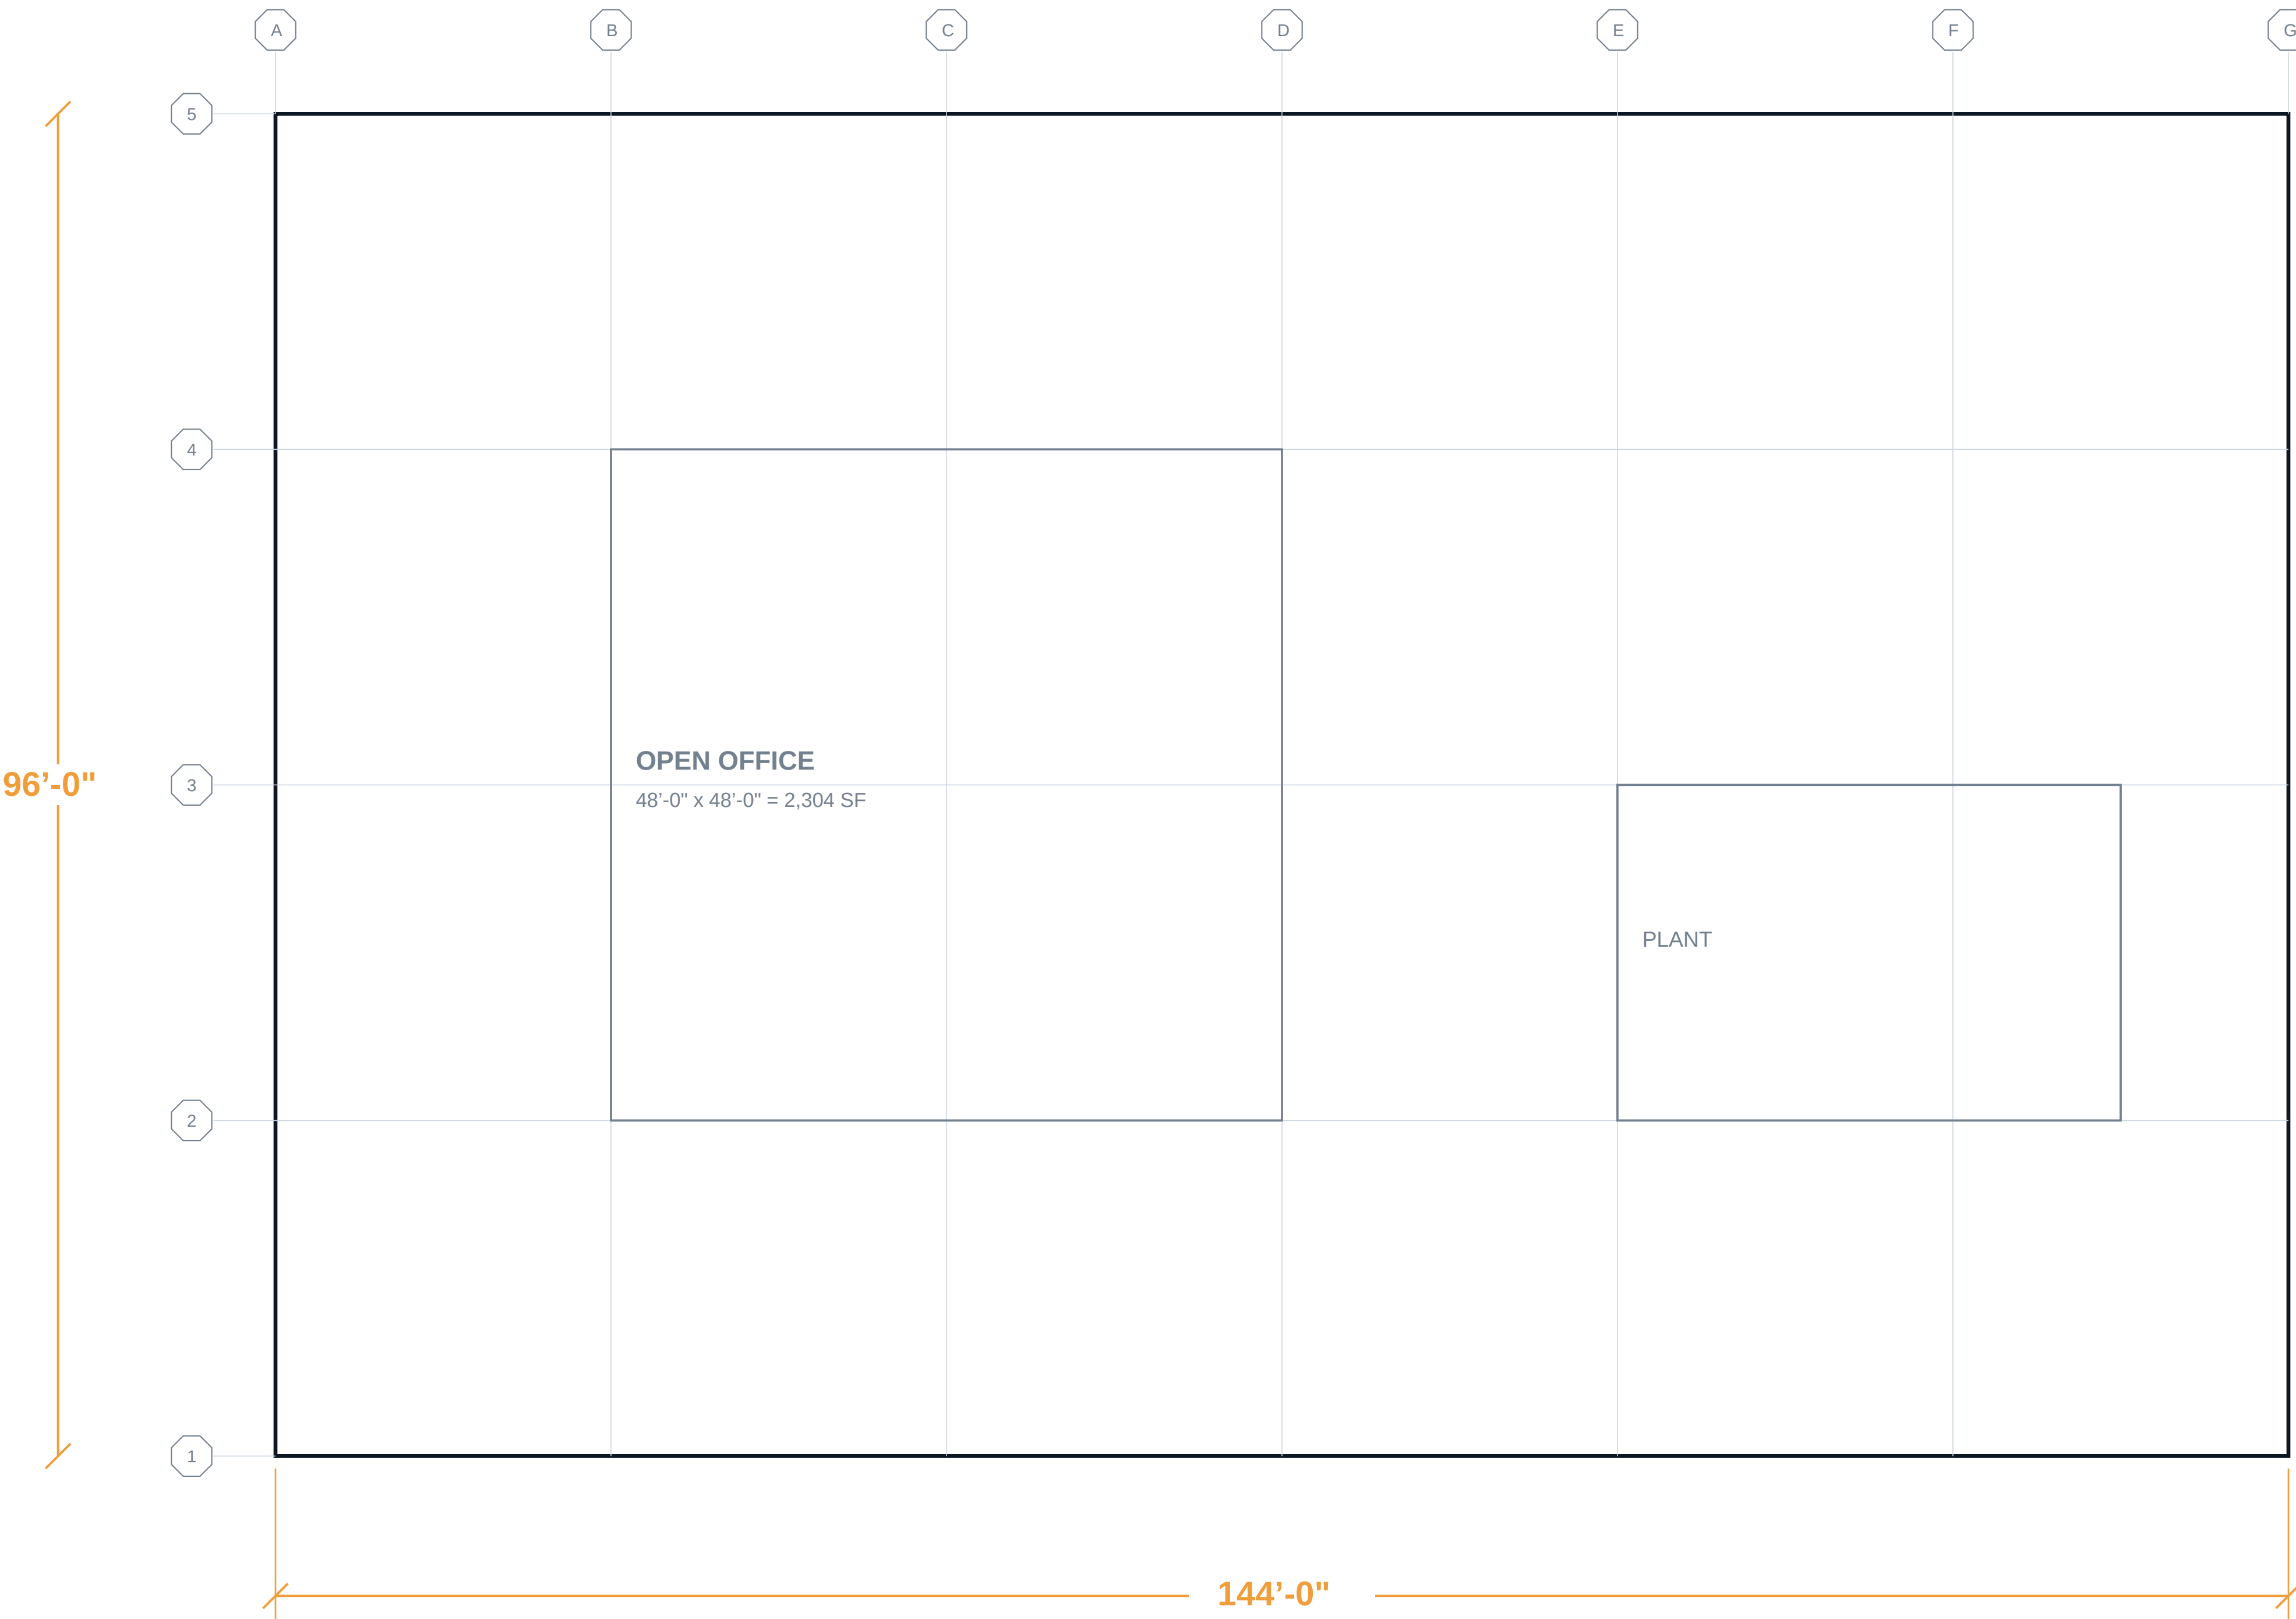

SheetForge
Construction drawing review

PROJECT
Tutorial - Riverside Tower

DRAWN BY
SheetForge

SCALE
1/8" = 1'-0"

DATE
Issued with this build

STATUS
Not for construction

REVISIONS		
REV	DATE	DESCRIPTION
A	-	Issued with the application

A-201

SECOND FLOOR PLAN